




LE CENTRE DE SANTE ET DU BIEN

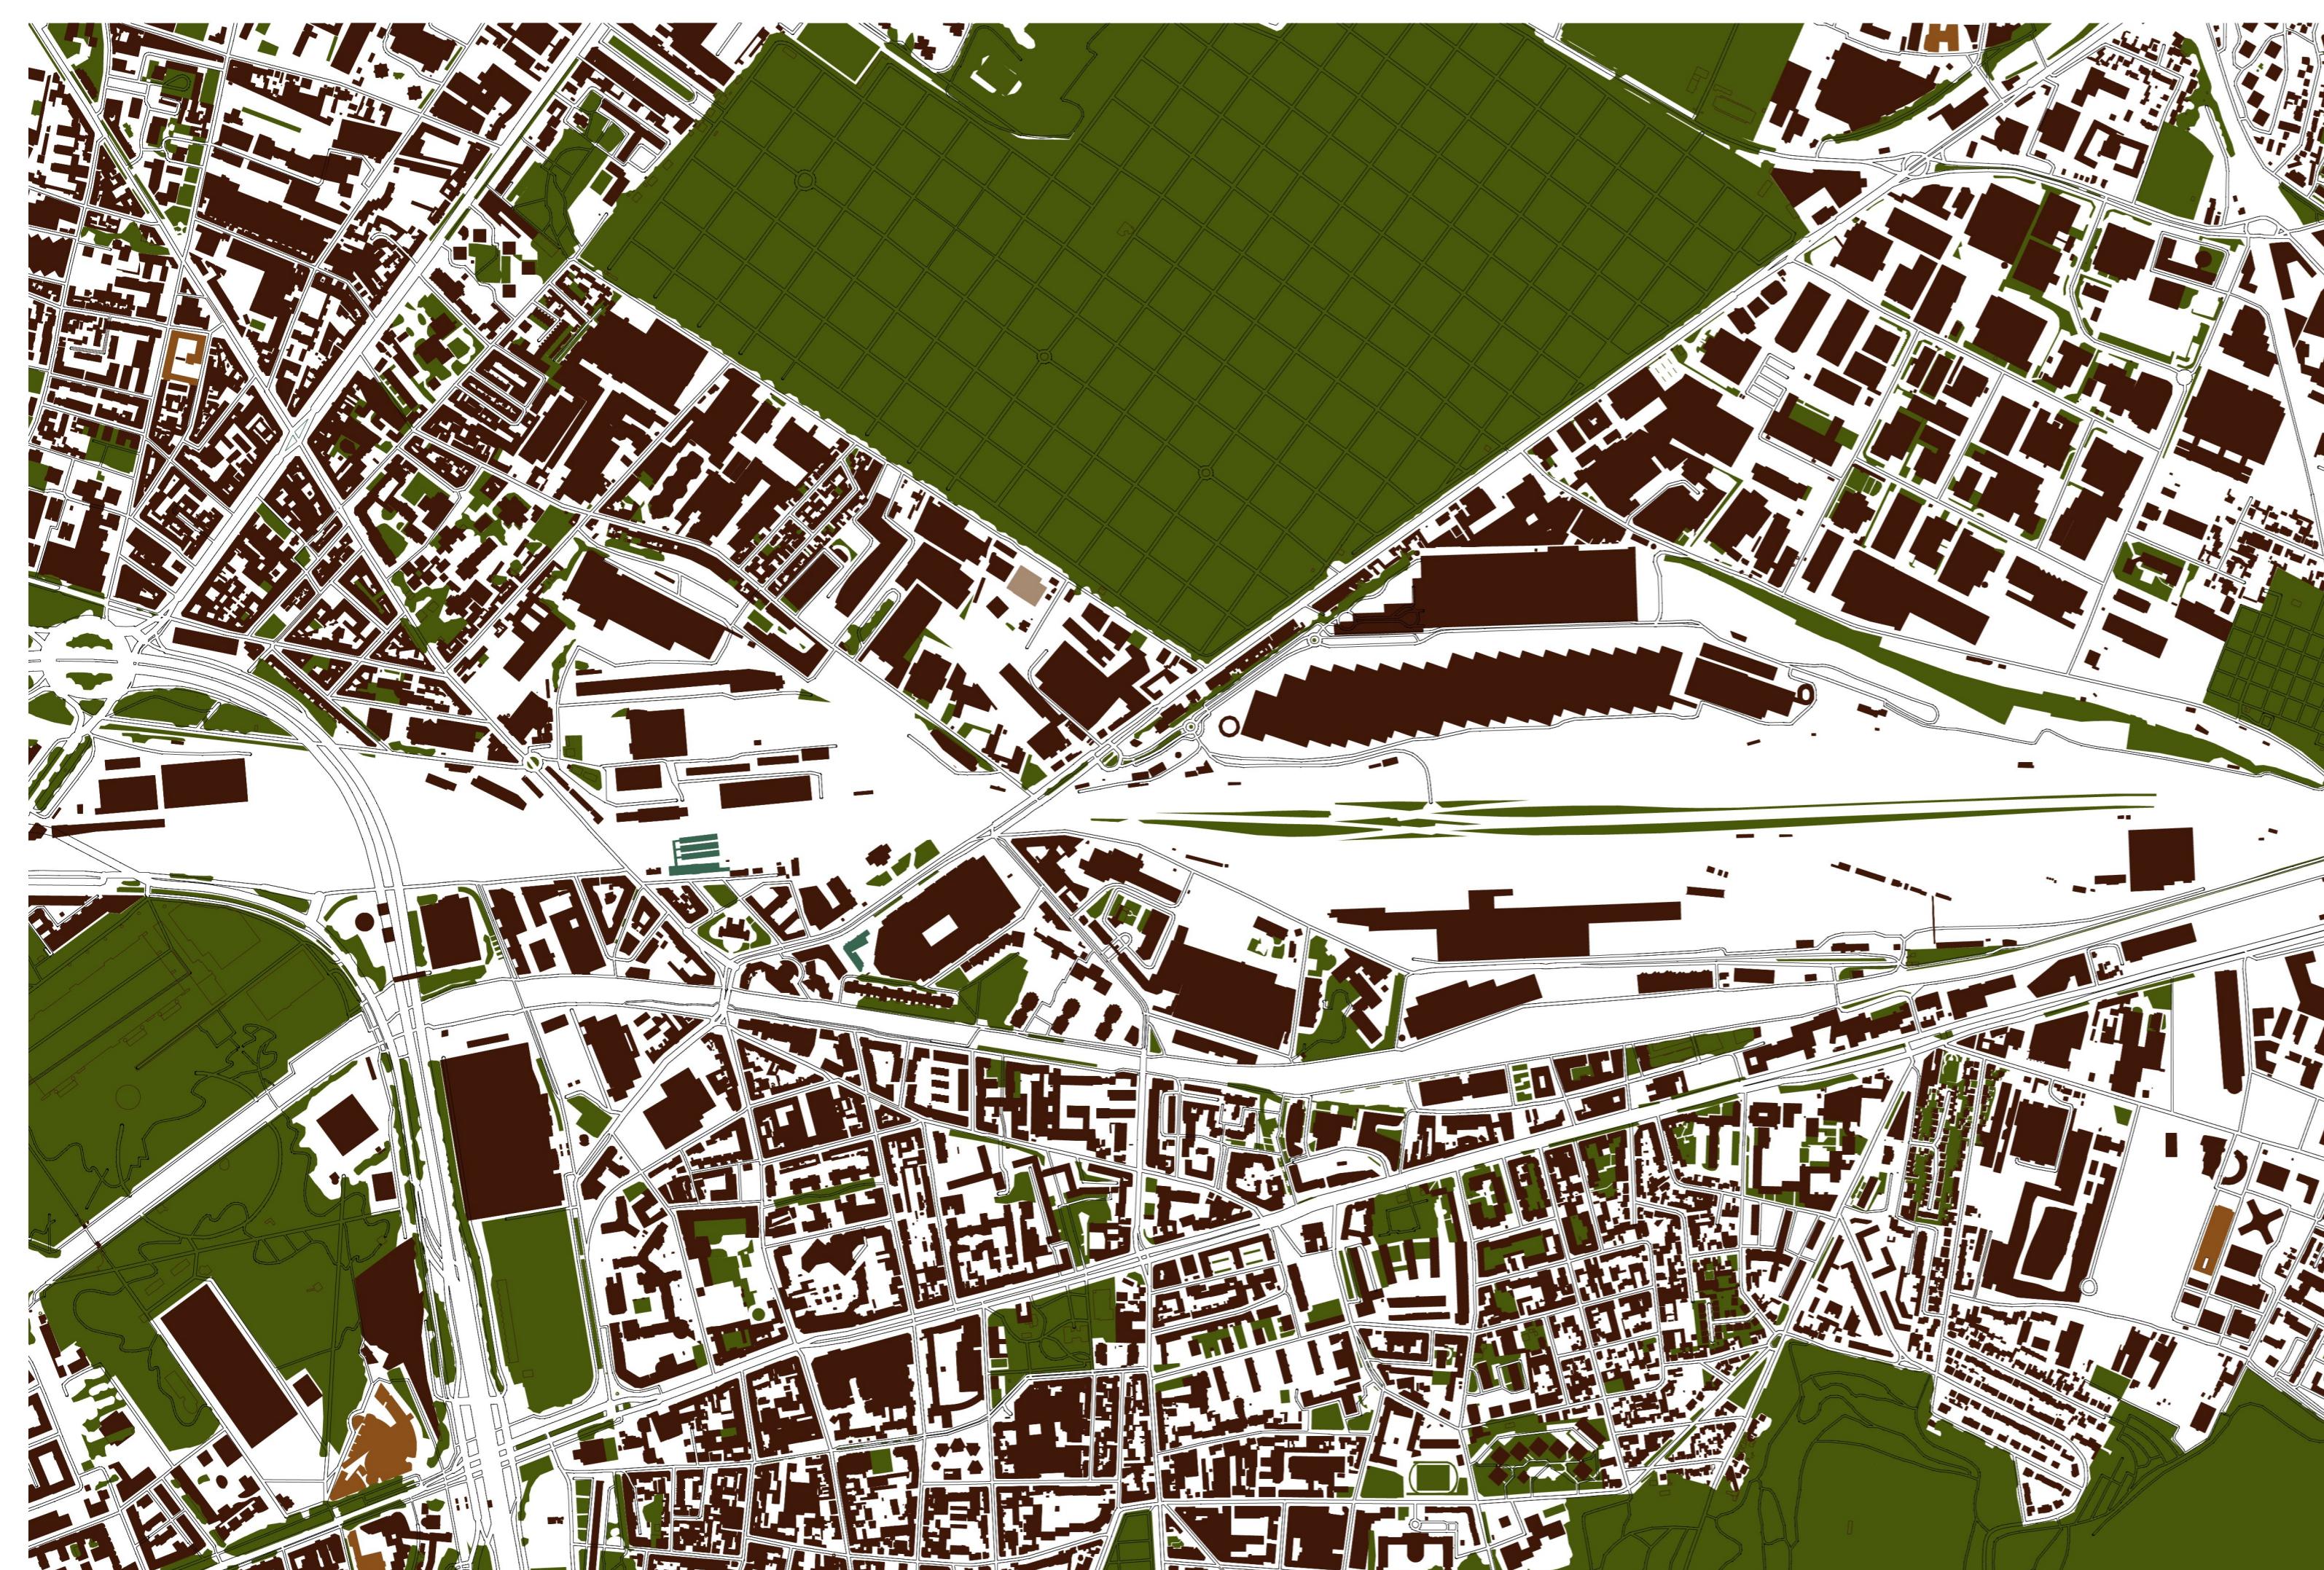

PLAN DE MASSE RDC 1/200

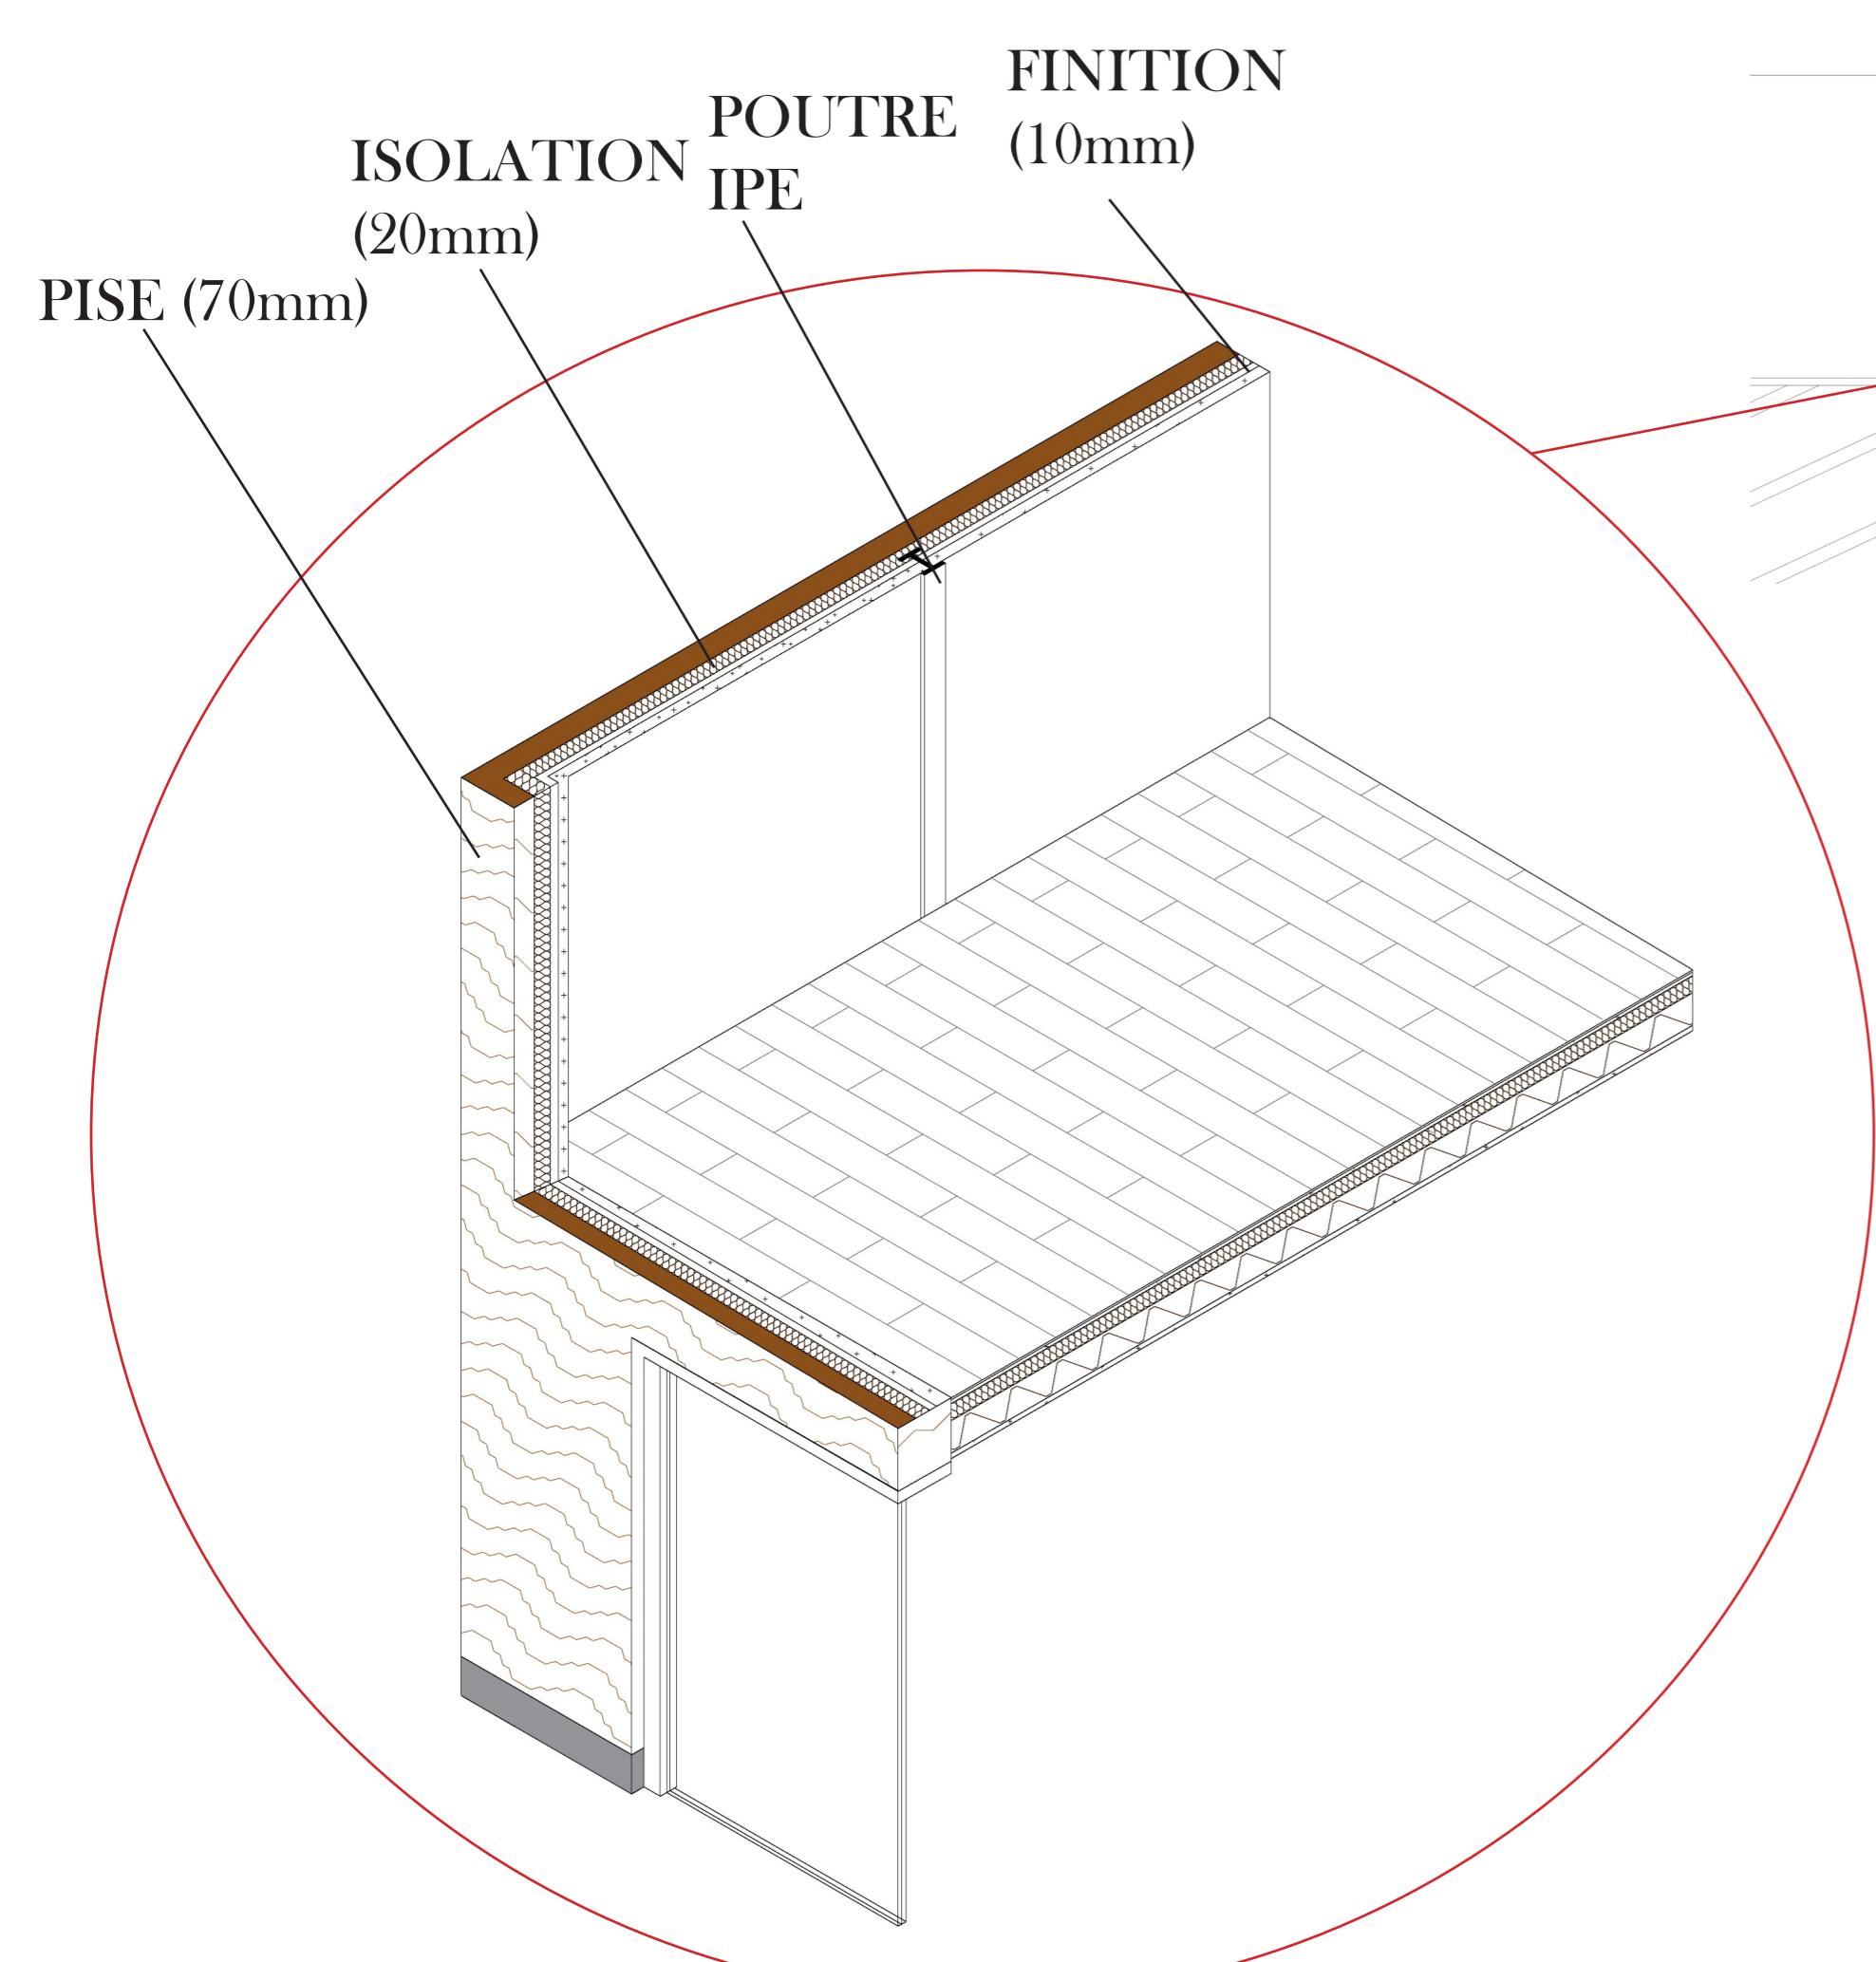

COUPE 1/200

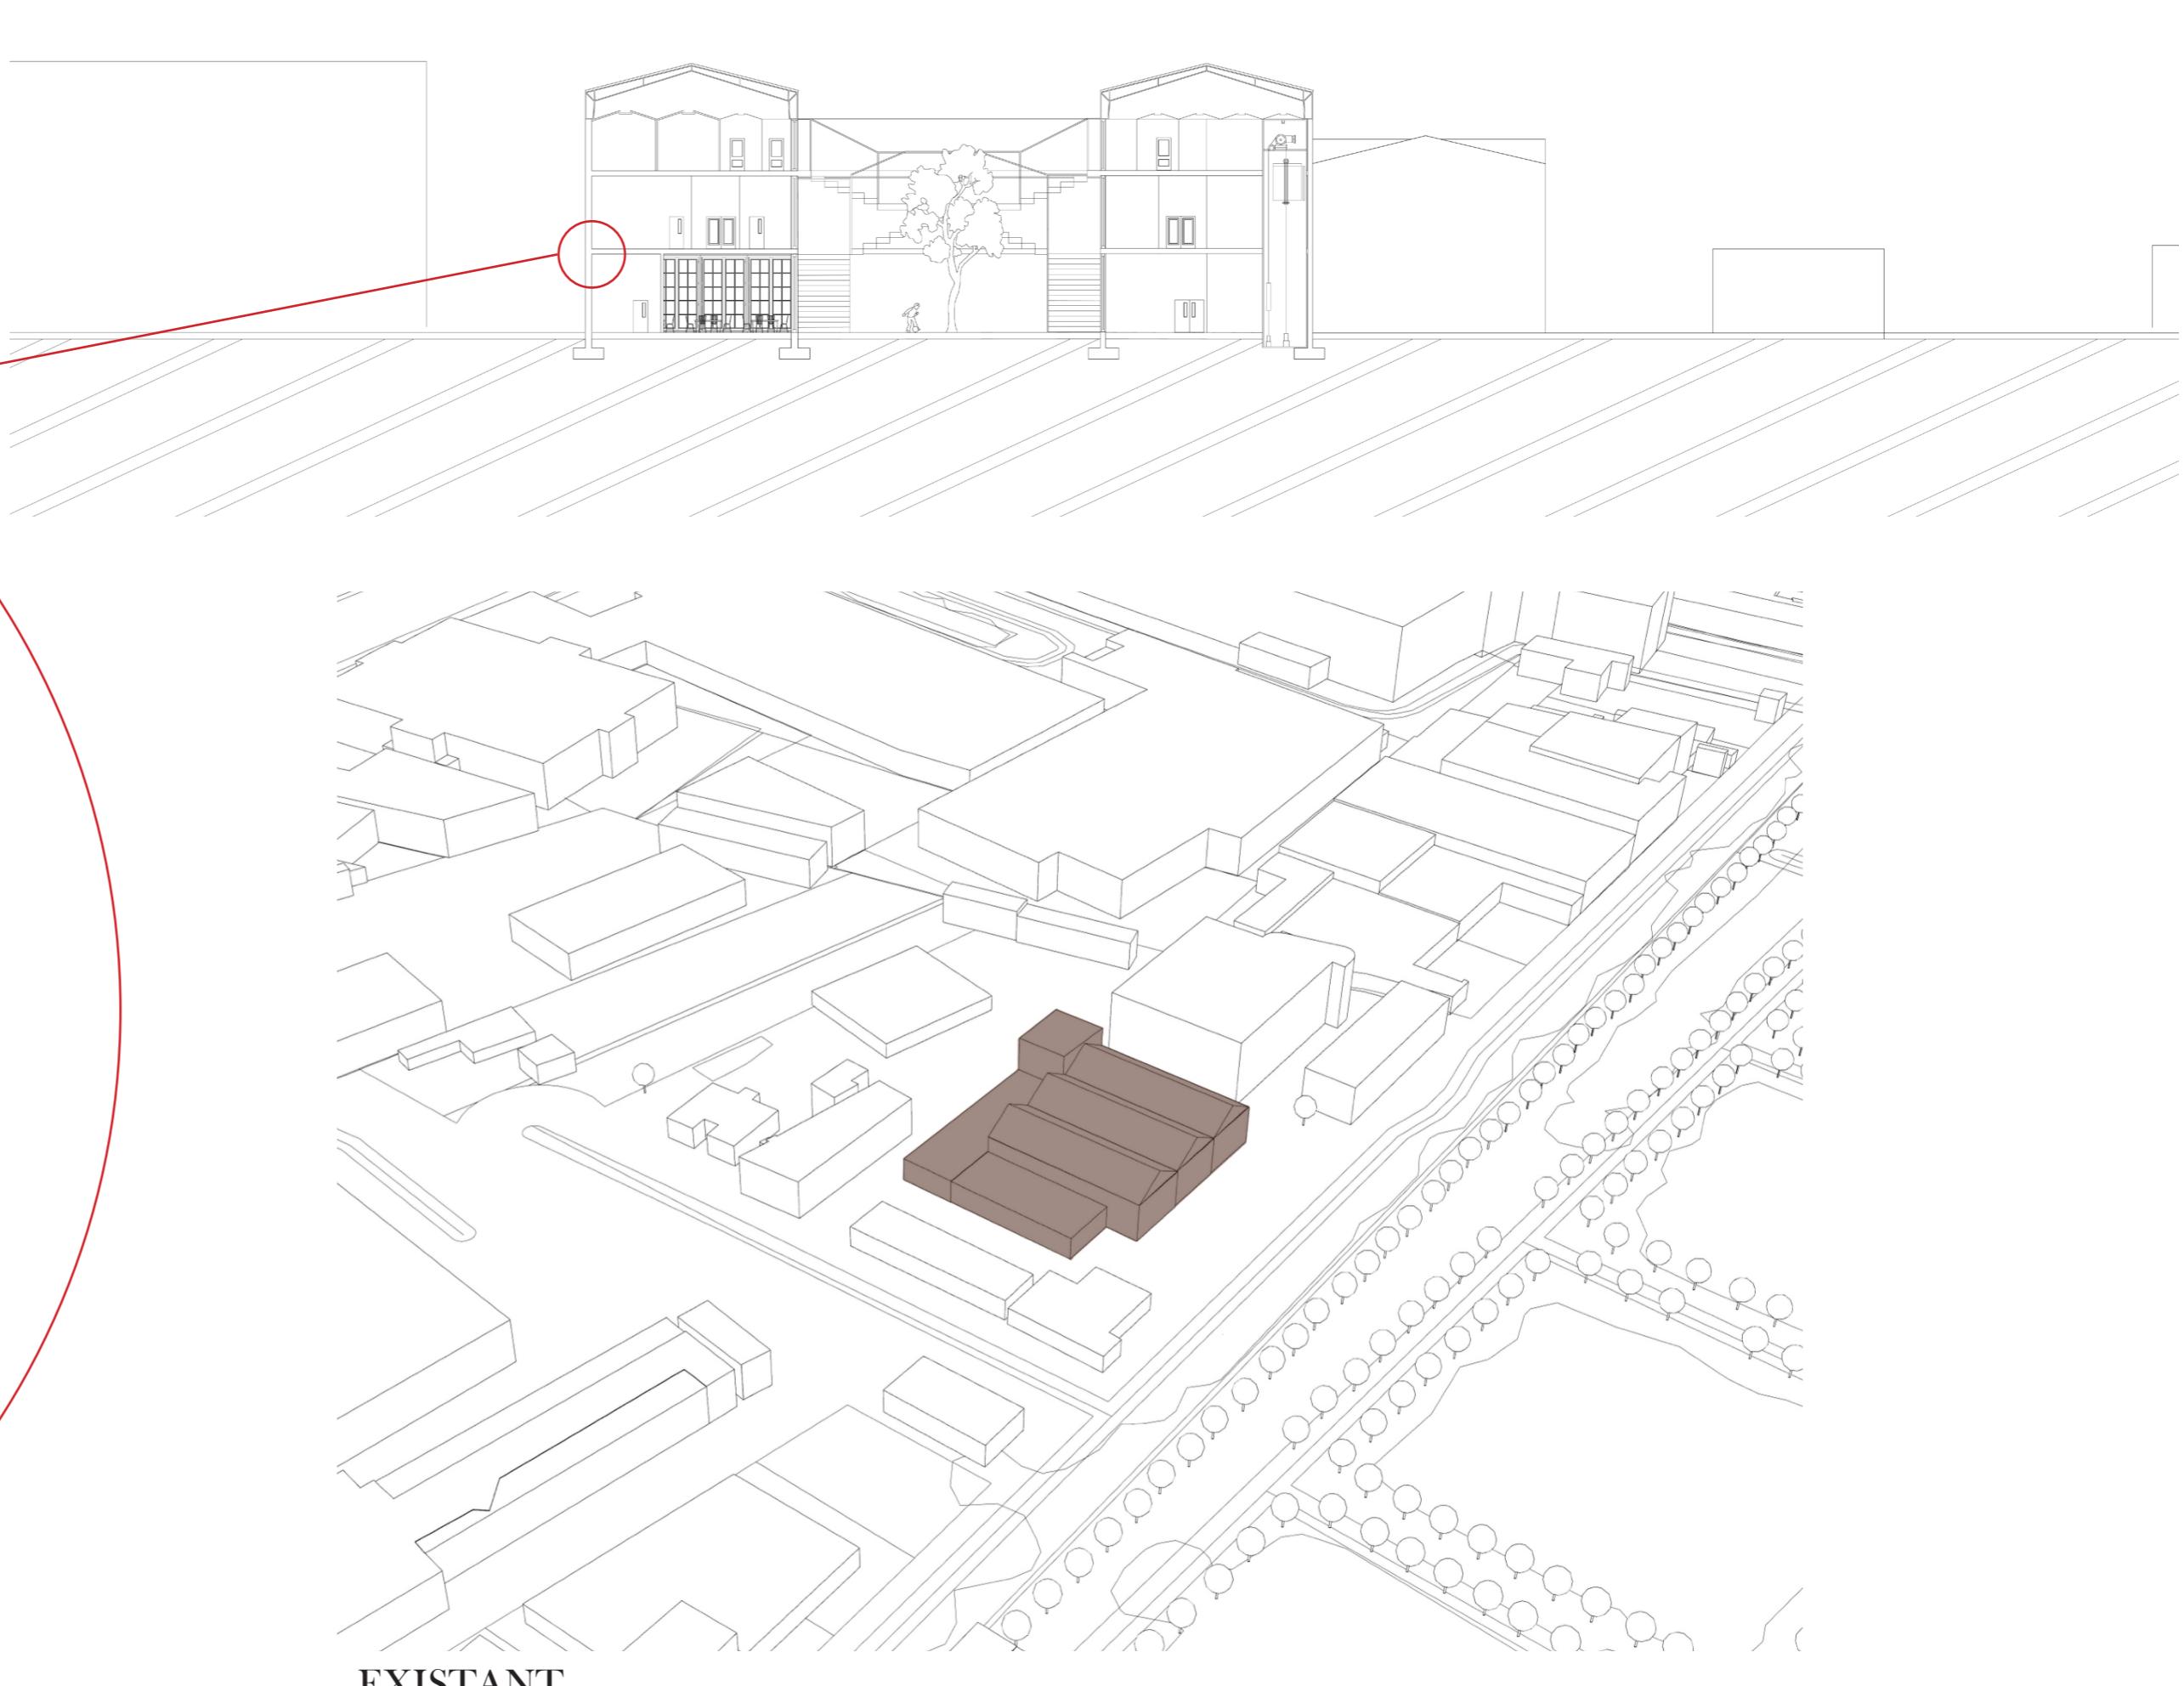

ETRE





ECLAIRAGE OPTIMAL




LE CALME/LA THERAPIE



DISCUTER/TRANSMISSION

SE REUNIR/LE RAPPORT A LA TERRE

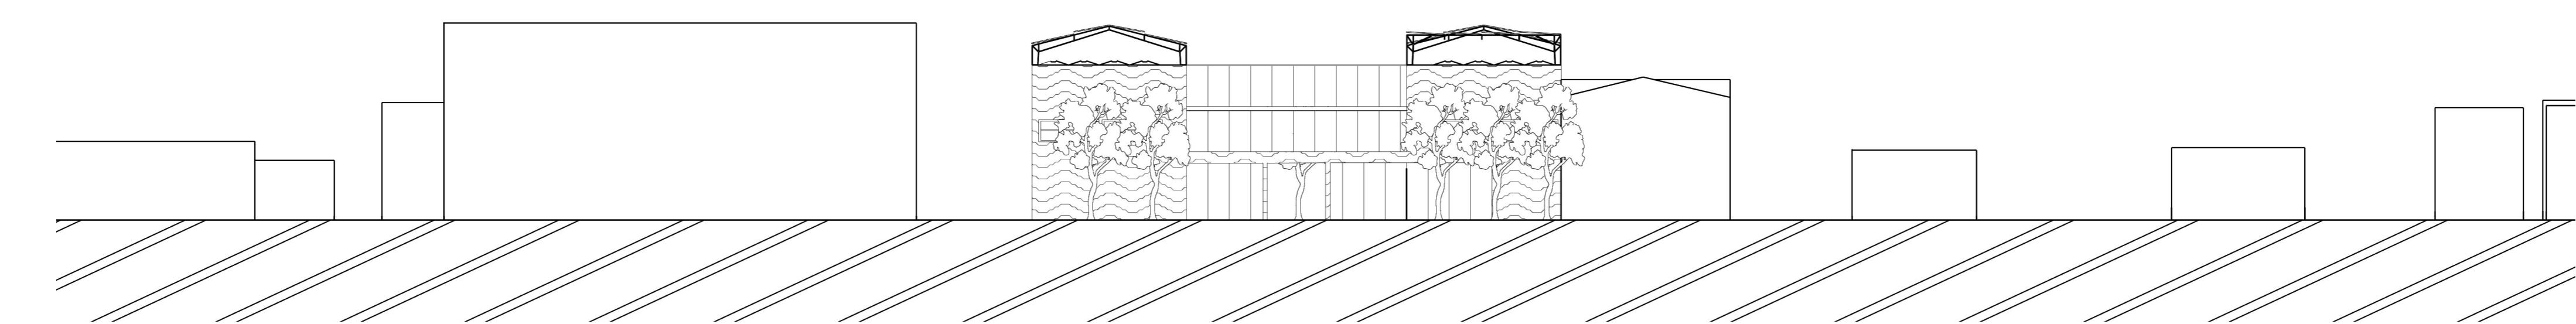
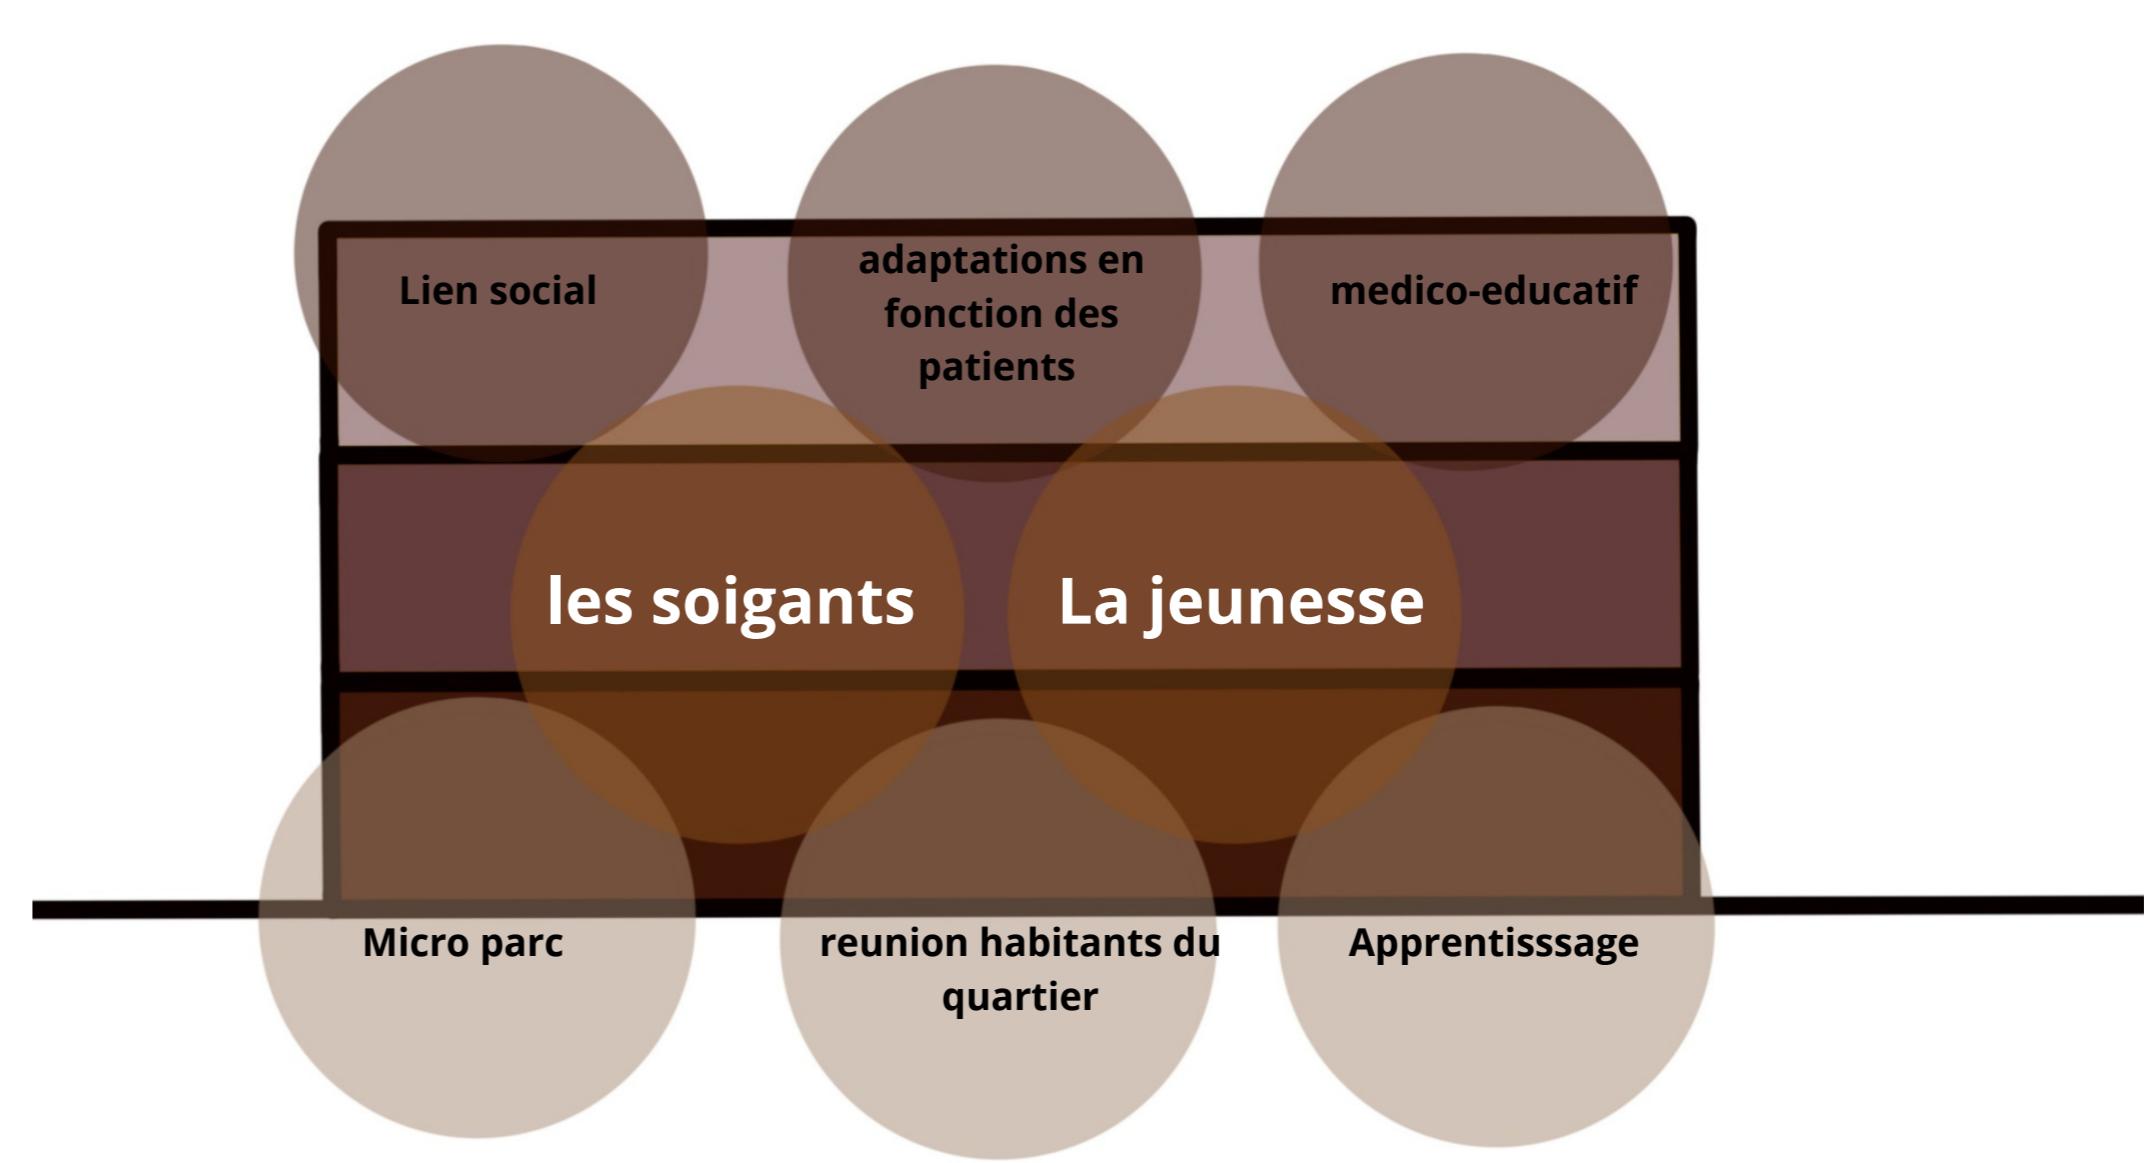


ELEVATION 1/500

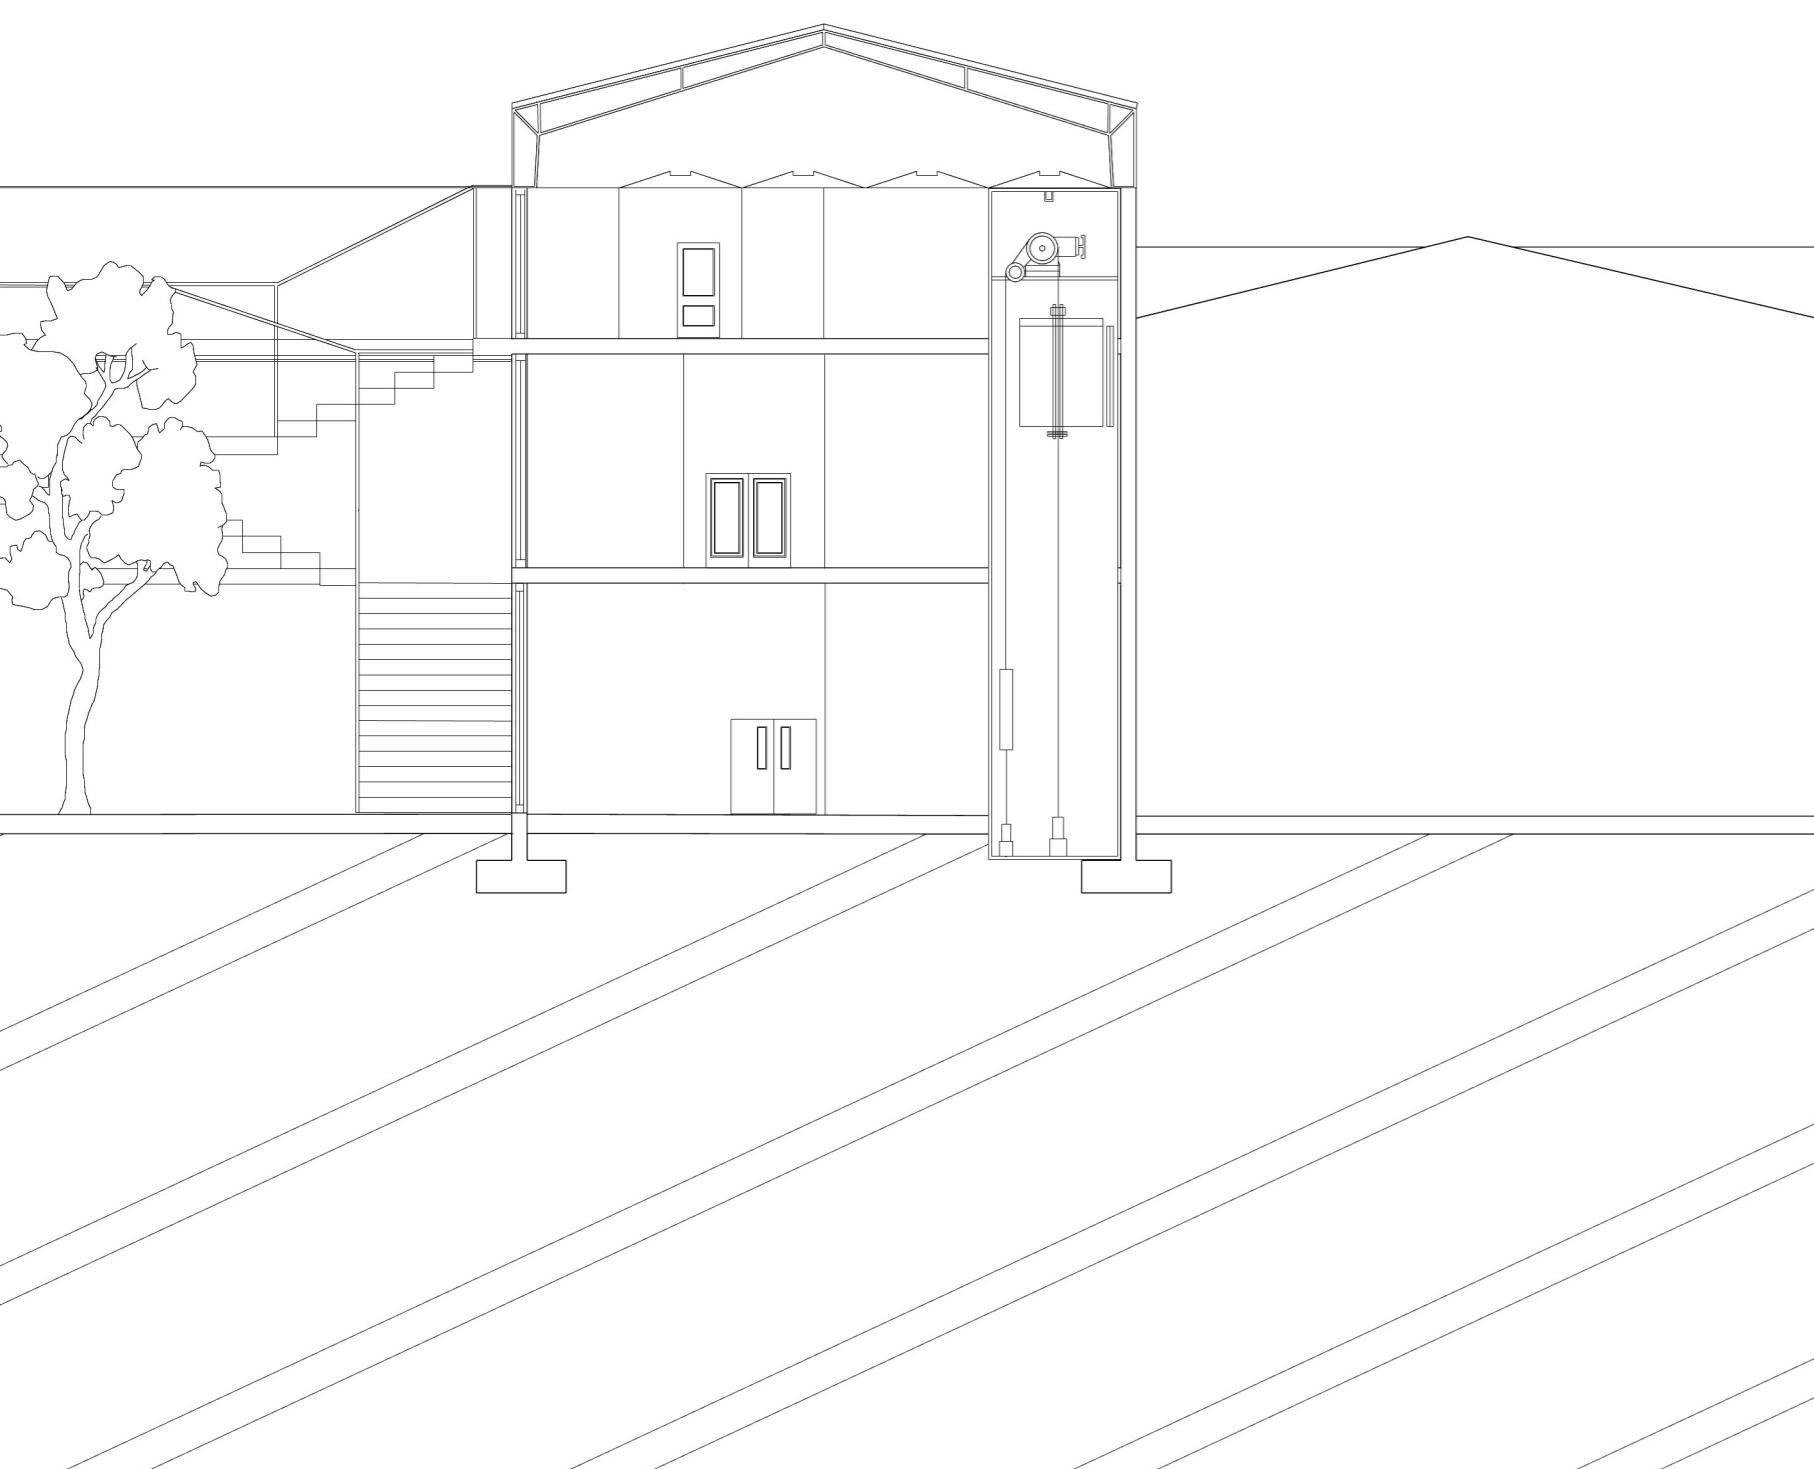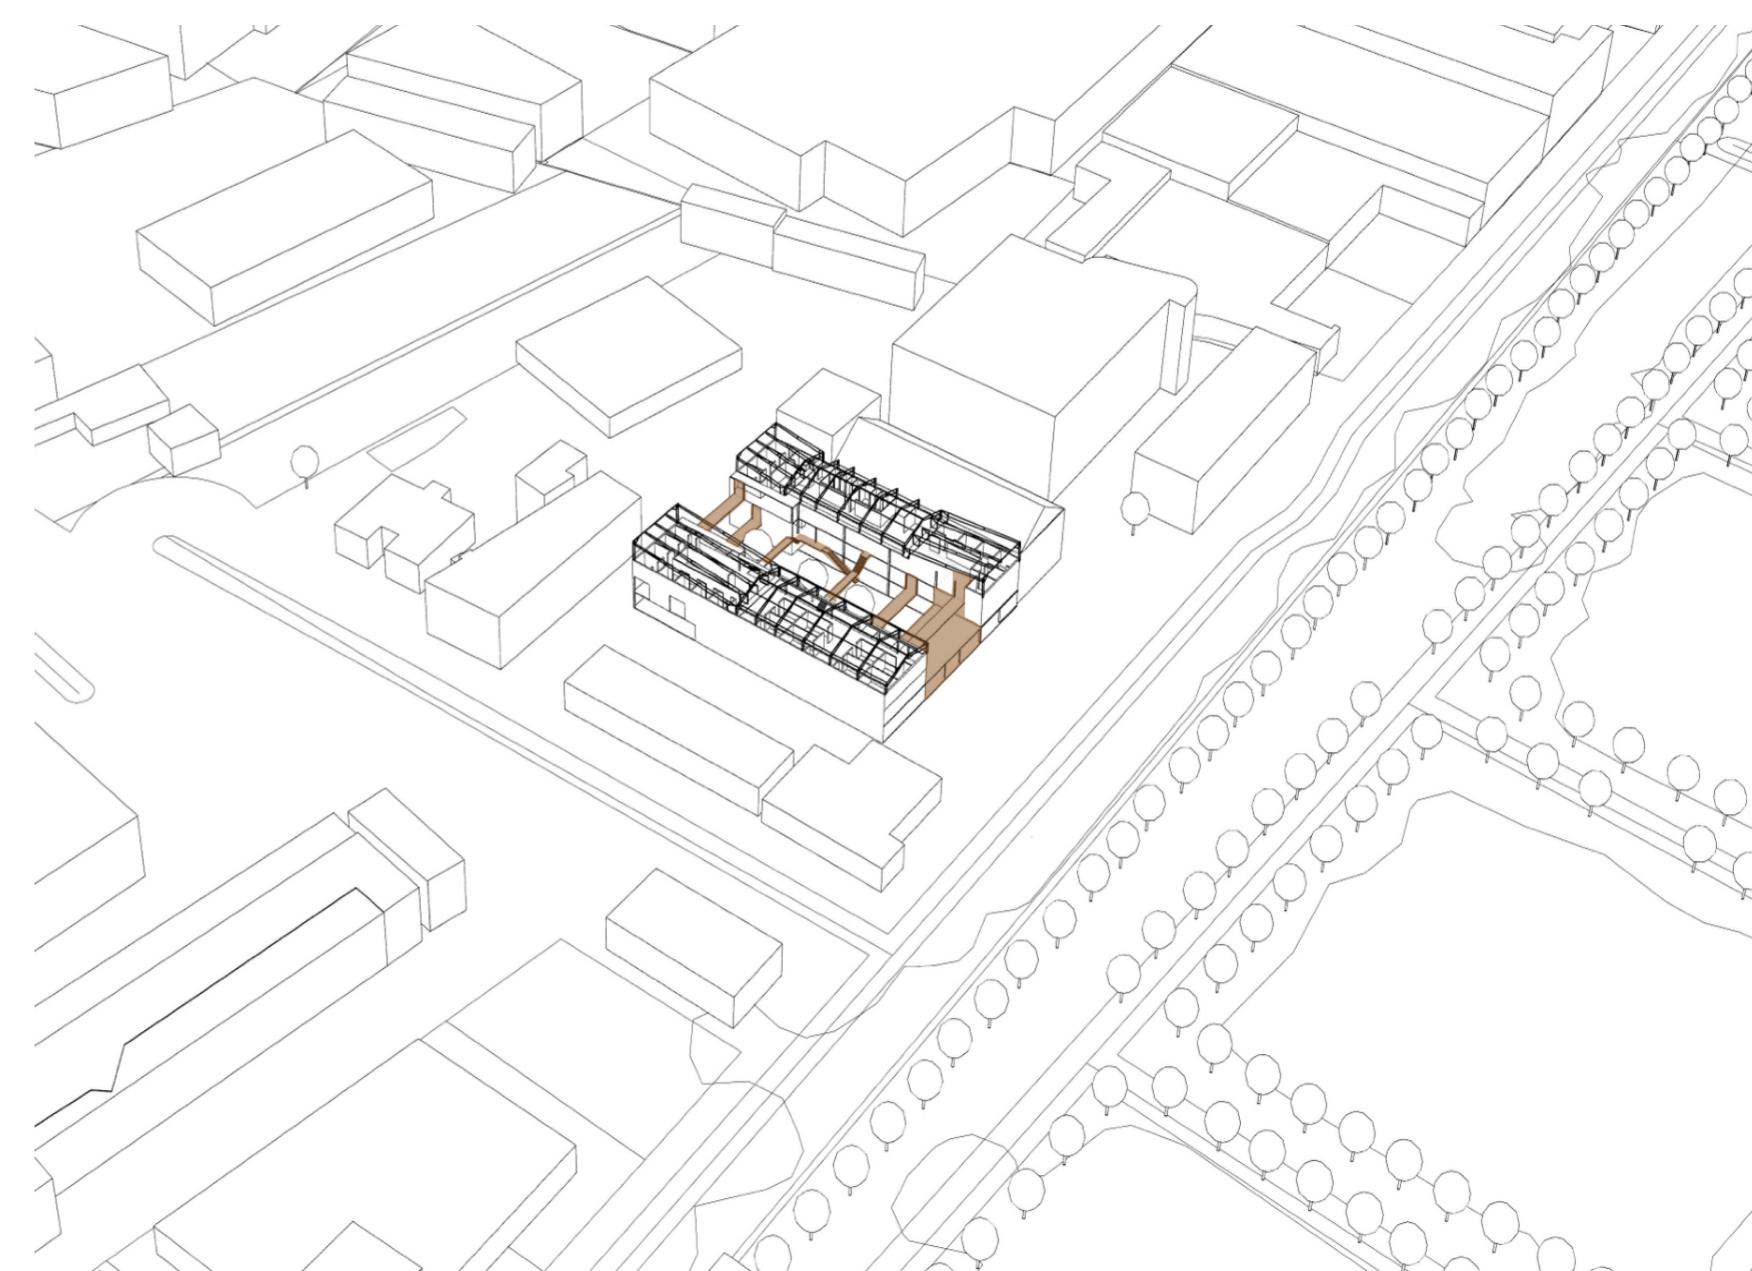
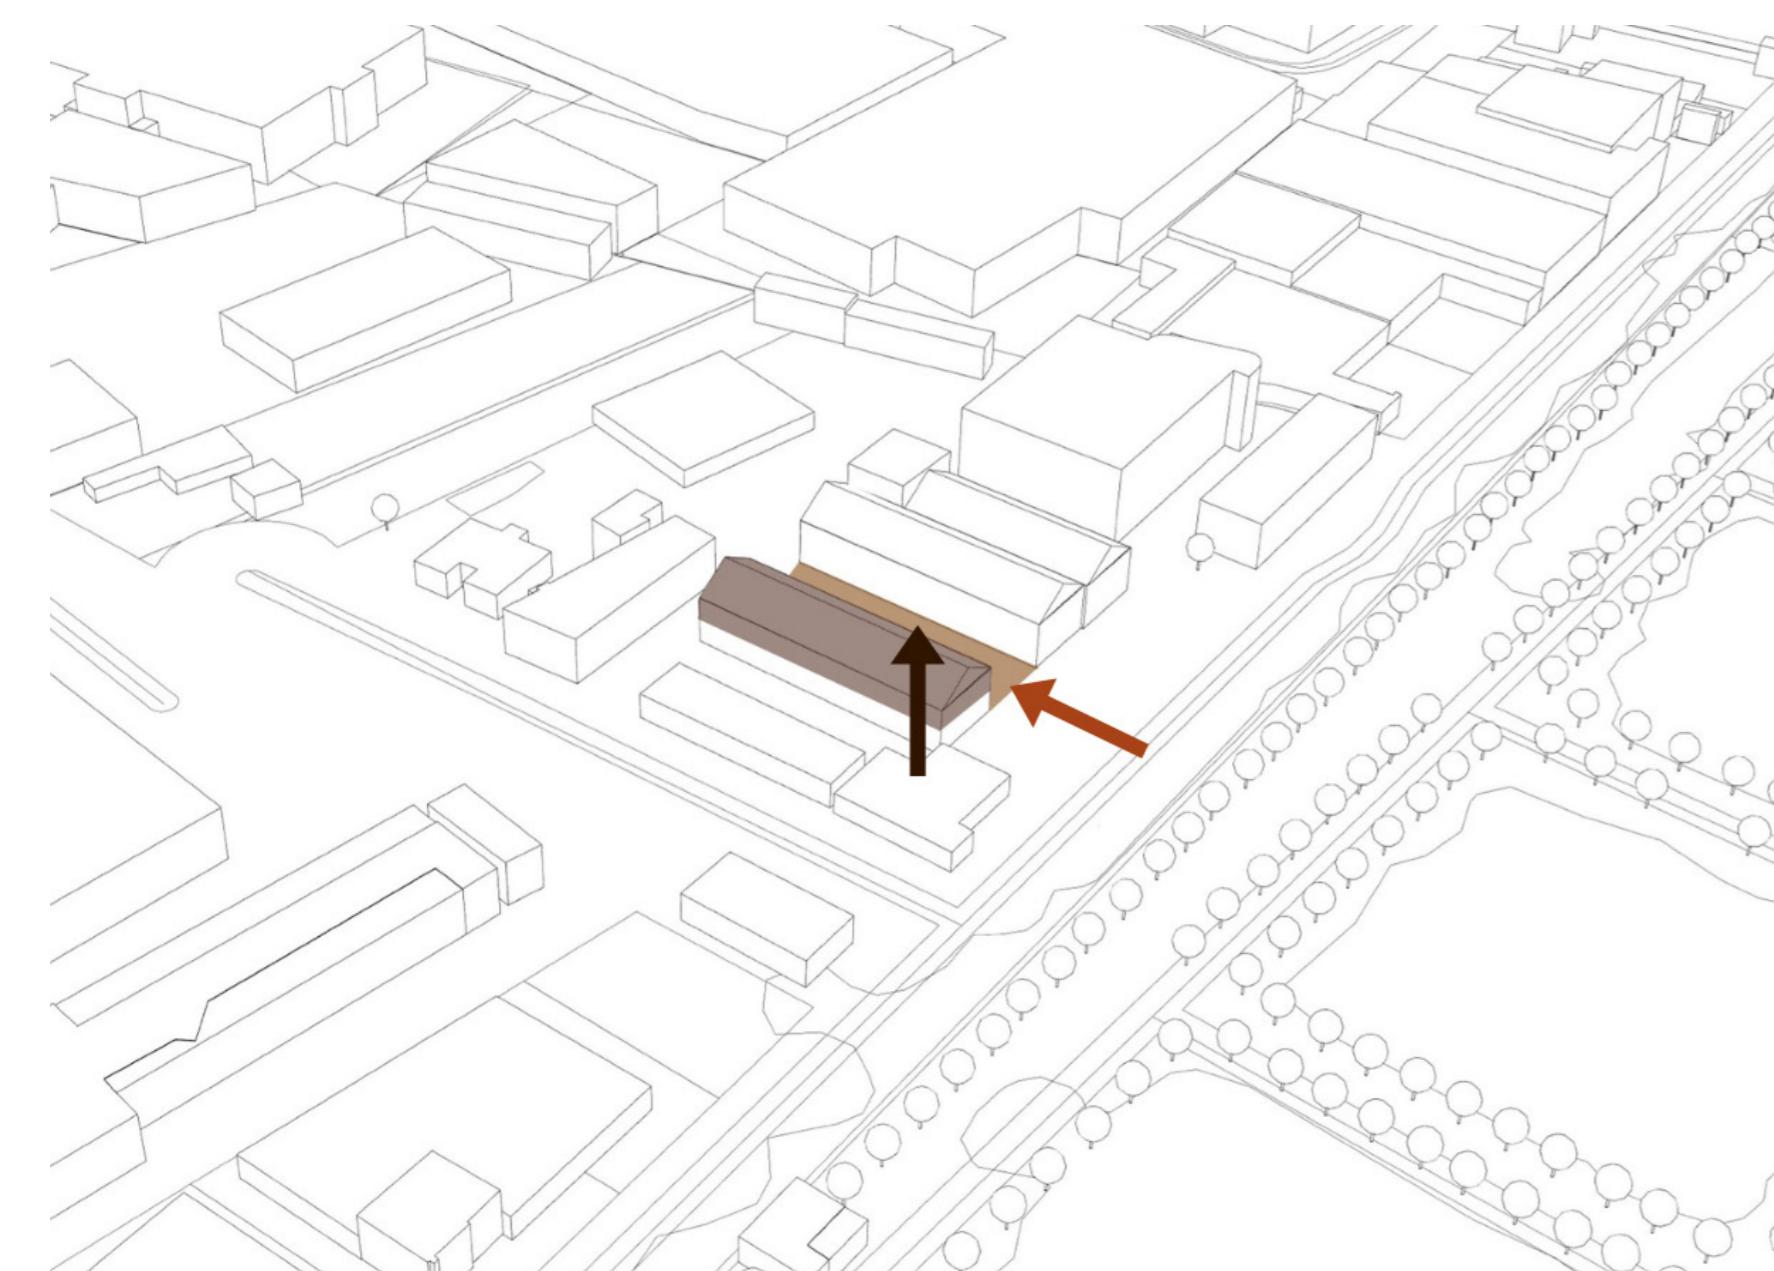


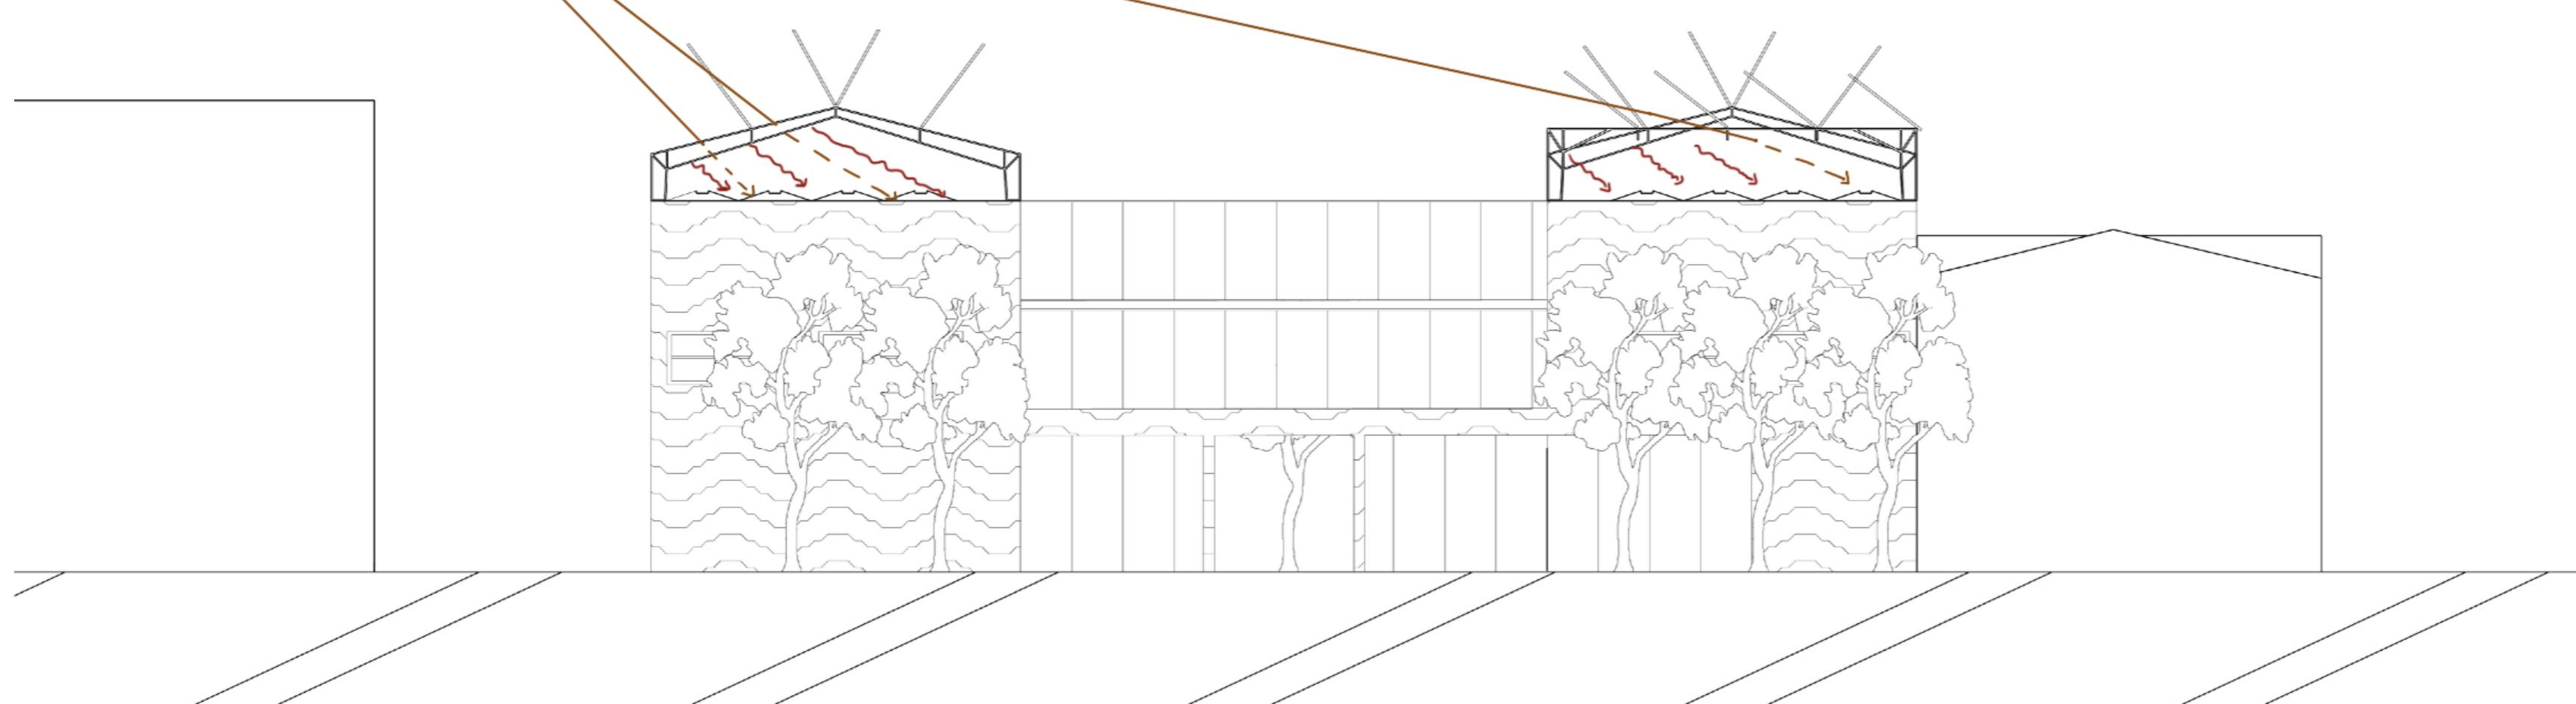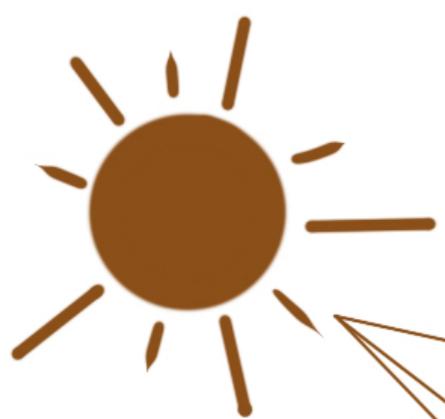

VOLETS DU TOIT
OUVERTS

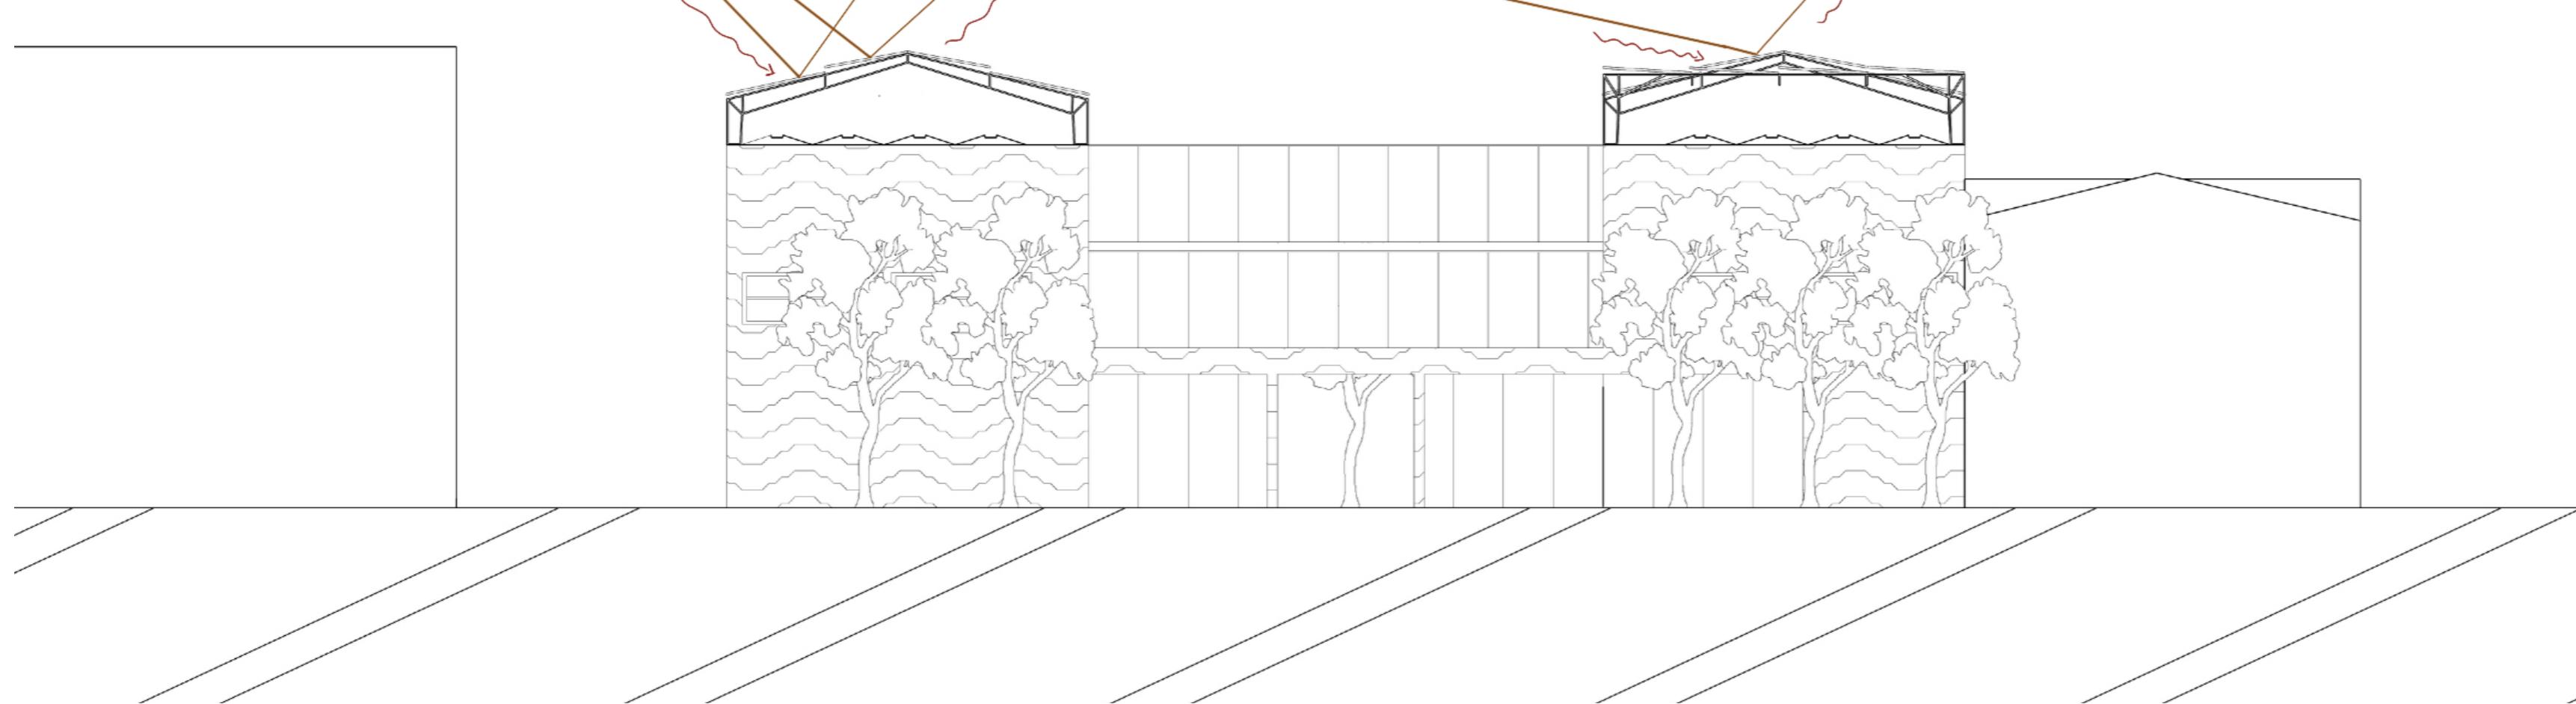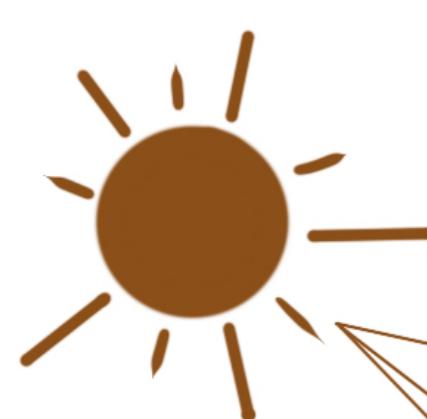

VOLETS DU TOIT-
FERMÉS

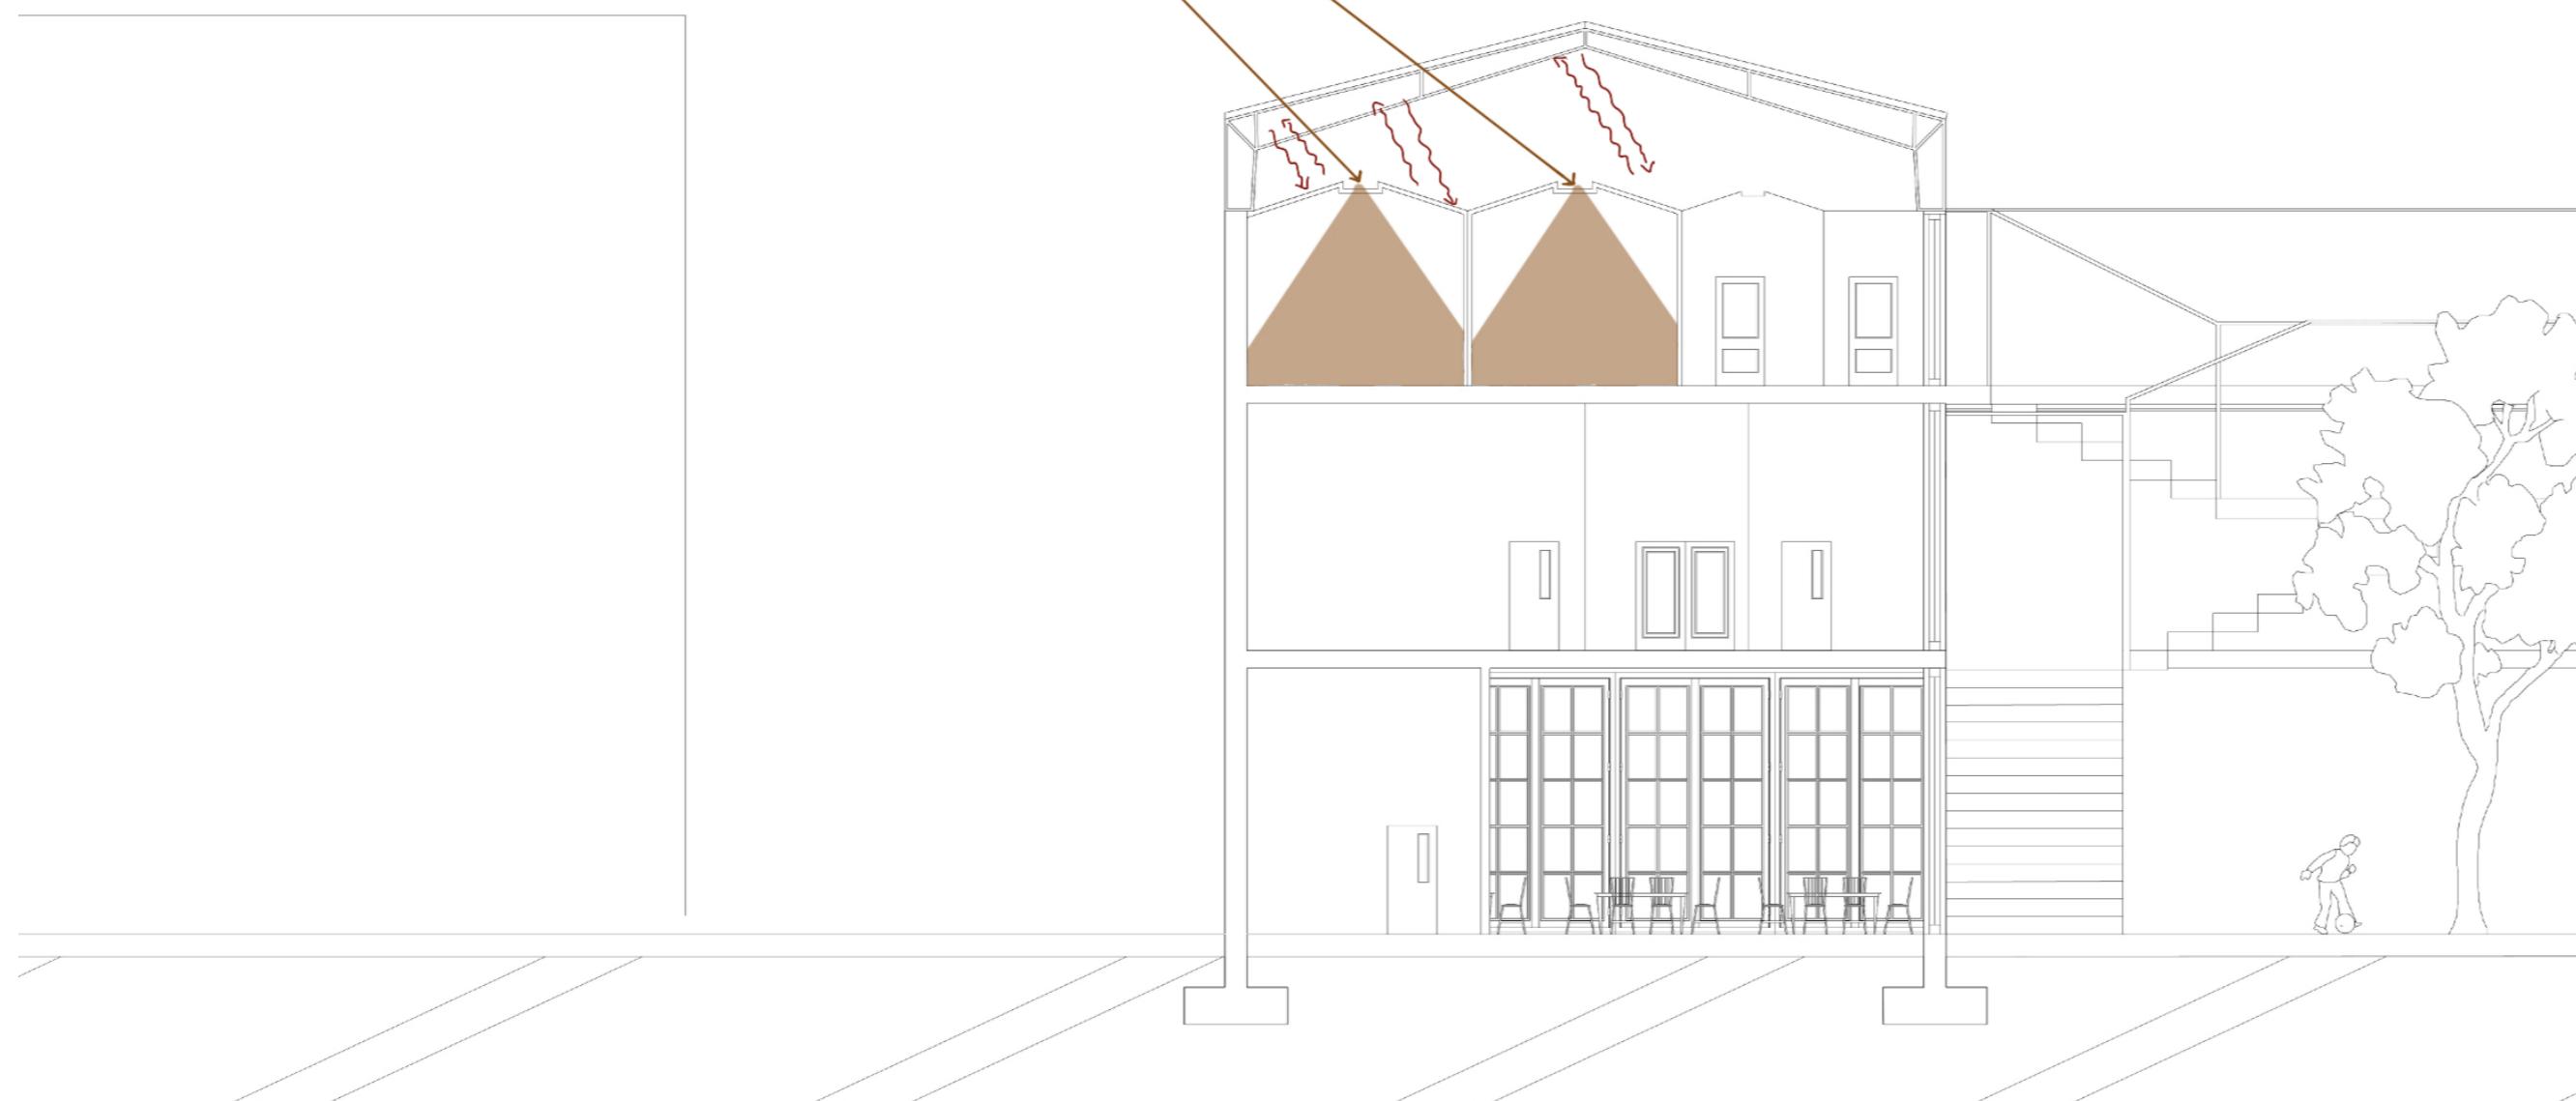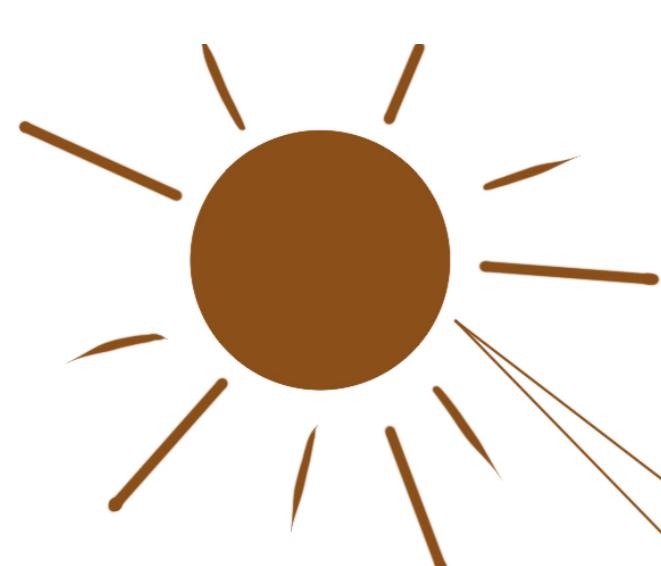

TUNNEL DE LUMIÈRE
DES PIÈCES PRIVES